Variante A:
Gartenweg bei 3 Häusern hinter dem 3,00m Grünstreifen
(d.h. bei 6 von 12 Häusern/Zeile)

Projekt	Planinhalt:	Bauherr:	Planverfasser:	
Lübeck-Travemünde Bebauungsplan 32.61.00 **"Neue Teutendorfer Siedlung"**	**Reihenhäuser BF 12.2** **Typ ERH 5,00m/MRH 6,00m** **Grundrisse Erdgeschoss** **Hs. 12.2-06 - Hs. 12.2-12**	bpd bouwfonds immobilienentwicklung **BPD Immobilienentwicklung GmbH** Region Nord Winterstraße 2; 22765 Hamburg; Tel.: +49 40 68 87 68-0 hamburg@bpd-de.de ..... Unterschrift	PWS Planungsgesellschaft Weber - Schmetzer mbH Hinrich-Thieß-Straße 46e; D-22844 Norderstedt; Tel.: (040) 526 82 771; pws@wtnet.de ..... Unterschrift	

Phase	Bereich	Teil	Index
100 - Konzept	**12.2**	**1a**	s.u.

Datum 23.05.2024
Index:
a
b
c
Maßstab/Größe: M 1:100 / 59,4x59,4

0 1 2 3 4 5 10 m

Variante B:
Gartenweg bei 3 Häusern hinter 0,8m-Hecke zzg. 2,20m
Grünstreifen hinter dem Weg (d.h. bei 6 von 12 Häusern/Zeile)

Projekt

Lübeck-Travemünde
Bebauungsplan 32.61.00
"Neue Teutendorfer Siedlung"

Planinhalt:

Reihenhäuser BF 12.2
Typ ERH 5,00m/MRH 6,00m
Grundrisse Erdgeschoss
Hs. 12.2-01 - Hs. 12.2-07

Bauherr:

bpd
bouwfonds immobilienentwicklung

BPD Immobilienentwicklung GmbH
Region Nord
Winterstraße 2; 22765 Hamburg;
Tel.: +49 40 68 87 68-0
hamburg@bpd-de.de

.....
Unterschrift

Planverfasser:

PWS

Planungsgesellschaft Weber - Schmetzer mbH
Hinrich-Thieß-Straße 46e; D-22844 Norderstedt;
Tel.: (040) 526 82 771; pws@wtnet.de

.....
Unterschrift

Phase	Bereich	Teil	Index
100 - Konzept	**12.2**	**1b**	s.u.

Datum 23.05.2024
Index:
a
b
c
Maßstab/Größe: M 1:100 / 59,4x59,4

0 1 2 3 4 5 10 m

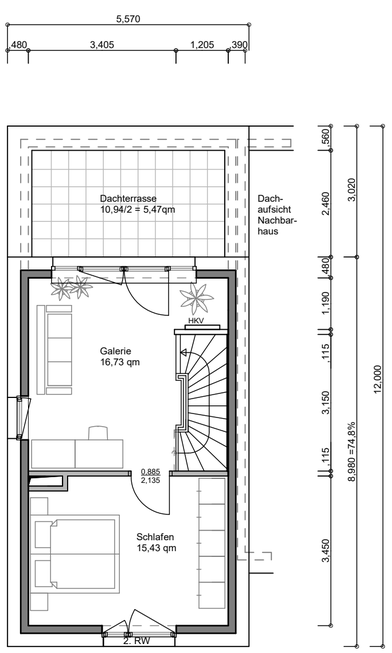

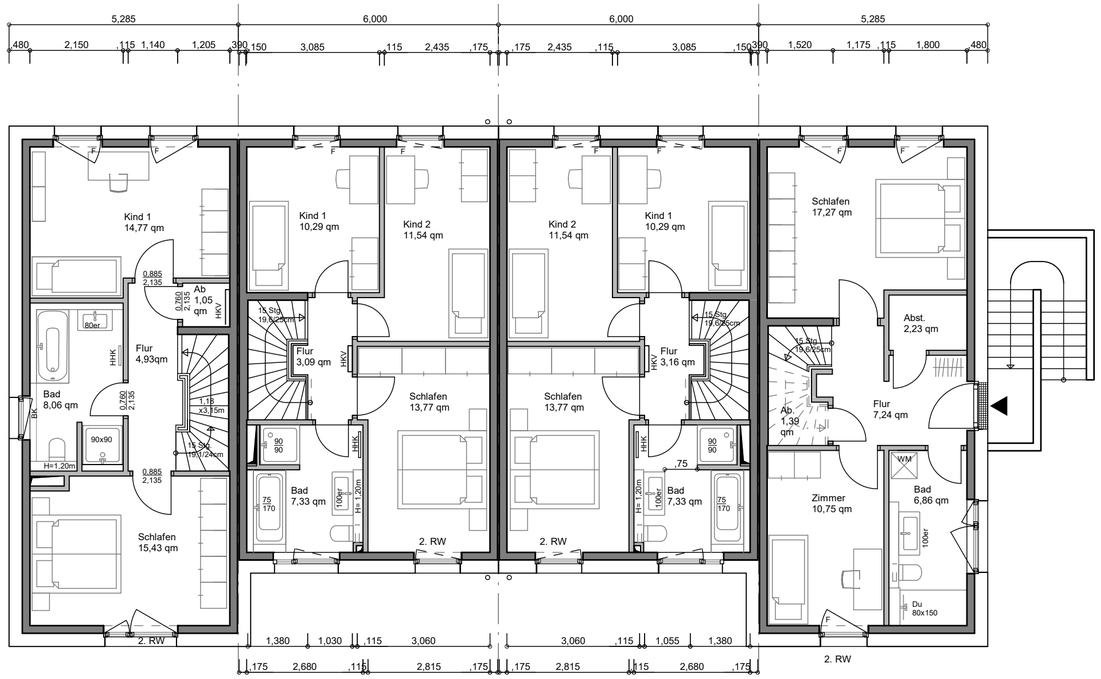

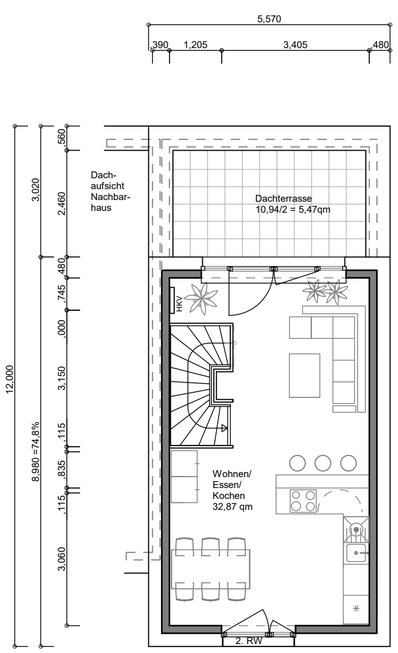

Staffel
Hs. 12.2-04

SG: 32,16 qm
+Dachterrasse
10,94/2 =5,47 qm

OG
Hs. 12.2-04

OG: 44,24 qm

ERH Ilg +Staffel
= 4-5- Zi.-WE
134,40 qm

OG
Hs. 12.2-03

OG: 46,02 qm

MRH Ilg
= 4- Zi.-WE
99,71 qm

OG
Hs. 12.2-02

OG: 46,02 qm

MRH Ilg
= 4- Zi.-WE
99,71 qm

OG
Hs. 12.2-01

ERH Ilg +Staffel
Beispiel
ERH mit Einlieger-WE

OG: 45,74 qm

OG+SG
= 3- Zi.-WE
84,08 qm

Staffel
Hs. 12.2-01

SG: 32,87 qm
+Dachterrasse
10,94/2 =5,47 qm

Projekt

Lübeck-Travemünde
Bebauungsplan 32.61.00
"Neue Teutendorfer Siedlung"

Planinhalt:

Reihenhäuser BF 12.2
Typ ERH 5,00m/MRH 6,00m
Grundrisse OG + Staffel

Bauherr:

bpd
bouwfonds immobilienentwicklung

BPD Immobilienentwicklung GmbH
Region Nord
Winterstraße 2; 22765 Hamburg;
Tel.: +49 40 68 87 68-0
hamburg@bpd-de.de

.....
Unterschrift

Planverfasser:

PWS

Planungsgesellschaft Weber - Schmetzer mbH
Hinrich-Thieß-Straße 46e; D-22844 Norderstedt;
Tel.: (040) 526 82 771; pws@wtnet.de

.....
Unterschrift

Phase	Bereich	Teil	Index
100 - Konzept	**12.2**	**1c**	s.u.

Datum 23.05.2024
Index:
a
b
c
Maßstab/Größe: M 1:100 / DIN A2

0 1 2 3 4 5 10 m

Variante A:
Gartenweg bei 3 Häusern hinter dem 3,00m Grünstreifen
(d.h. bei 6 von 12 Häusern/Zeile)

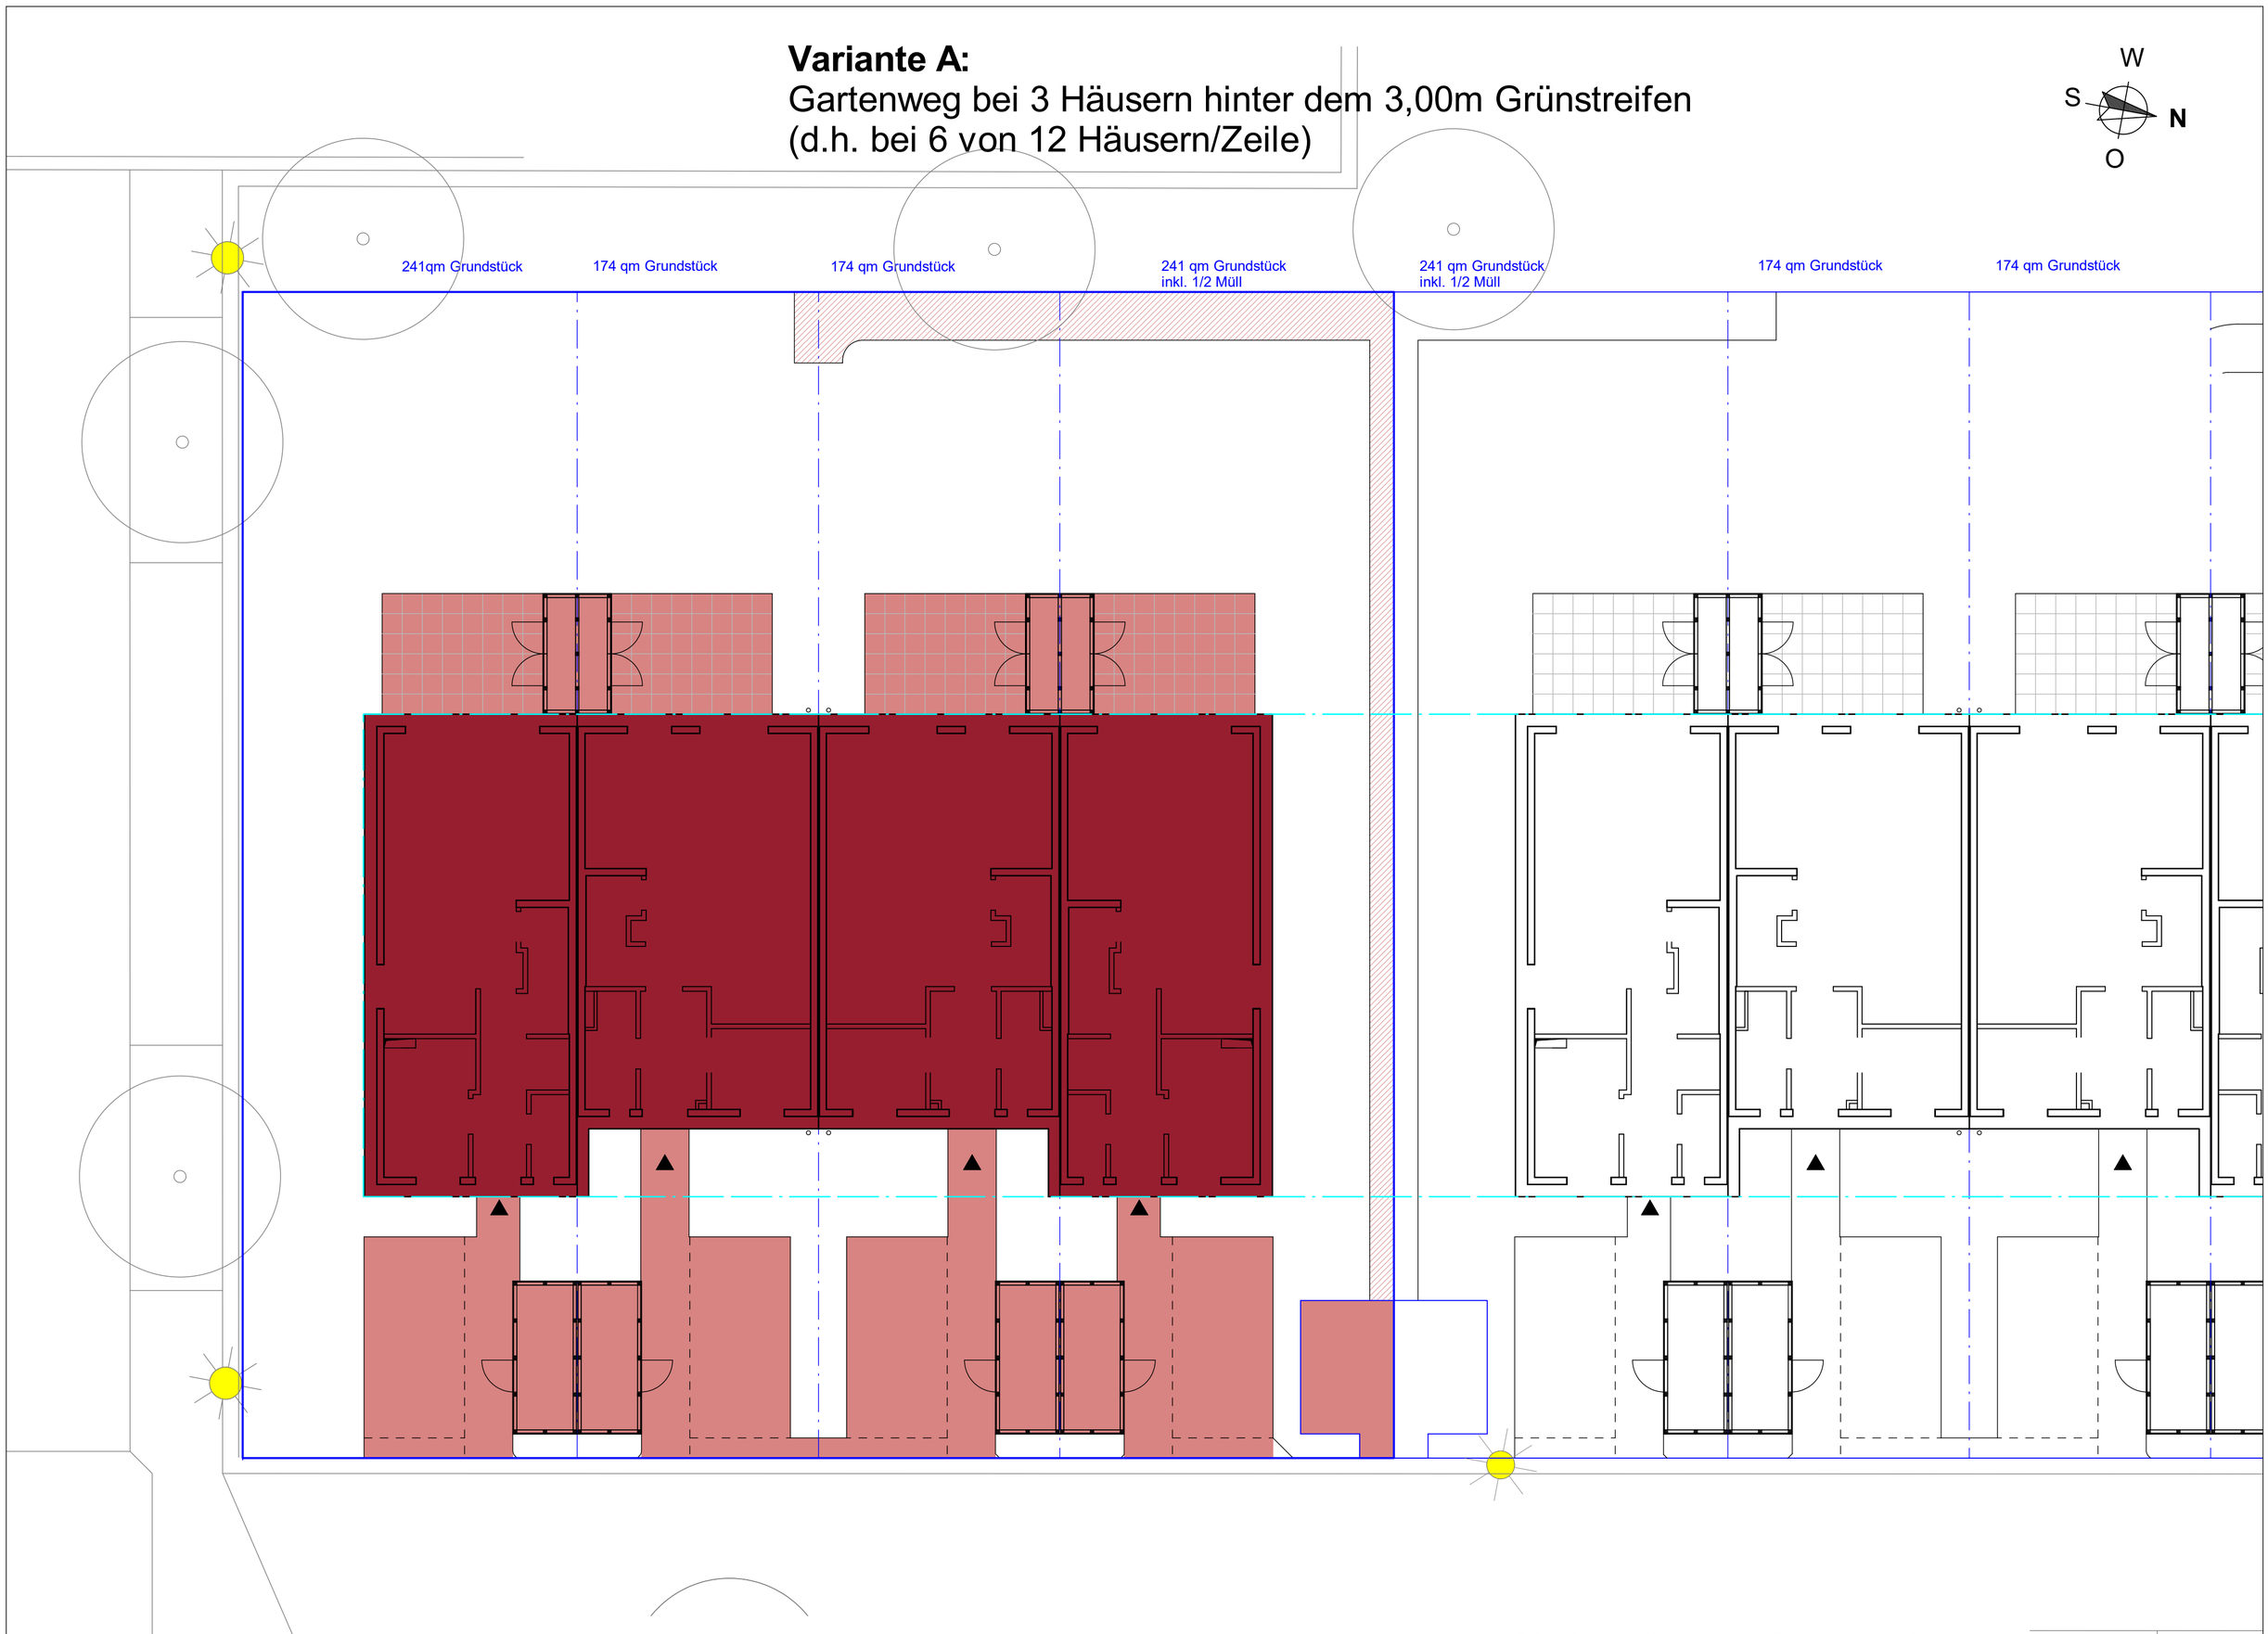

Grundstück	241 qm
GR Hauptgebäude	63,4 qm
GRZ 1 Hauptgebäude	**=0,26**
GR Hauptgebäude + Terr.	=75,4 qm
GRZ Hauptgebäude + Terr.	**=0,31**
Stellplatz/Zufahrt	13,8 qm
Zuwegung	7,9 qm
Schuppen bei Terrasse	2,6 qm
Gartenschuppen	6,1 qm
GR gesamt	=105,8 qm
GRZ 2	**=0,44**

Grundstück	174 qm
GR Hauptgebäude	62,3 qm
GRZ 1 Hauptgebäude	**=0,36**
GR Hauptgebäude + Terr.	=74,3 qm
GRZ Hauptgebäude + Terr.	**=0,43**
Stellplatz/Zufahrt	14,1 qm
Zuwegung	9,9 qm
Schuppen bei Terrasse	2,6 qm
Gartenschuppen	6,1 qm
GR gesamt	=107,0 qm
GRZ 2	**=0,615**

Grundstück	174 qm
GR Hauptgebäude	62,3 qm
GRZ 1 Hauptgebäude	**=0,36**
GR Hauptgebäude + Terr.	=74,3 qm
GRZ Hauptgebäude + Terr.	**=0,43**
Stellplatz/Zufahrt	14,1 qm
Zuwegung	9,9 qm
Schuppen bei Terrasse	2,6 qm
Gartenschuppen	6,1 qm
GR gesamt	=107,0 qm
GRZ 2	**=0,615**

Grundstück	241 qm
GR Hauptgebäude	63,4 qm
GRZ 1 Hauptgebäude	**=0,26**
GR Hauptgebäude + Terr.	=75,4 qm
GRZ Hauptgebäude + Terr.	**=0,31**
Stellplatz/Zufahrt	13,8 qm
Zuwegung	7,9 qm
Schuppen bei Terrasse	2,6 qm
Gartenschuppen	6,1 qm
Müllplatz (1/2)	8,2 qm
GR gesamt	=114,0 qm
GRZ 2	**=0,47**

Zeile 12.2-09 - 12.2-12
ohne Gartenweg

Grundstück	830 qm
GR Hauptgebäude	251,5 qm
GRZ 1 Hauptgebäude	**=0,30**
GR Hauptgeb. + Terr.	=299,4 qm
GRZ Hauptgebäude + Terr.	**=0,36**
Stellplätze/Zufahrten	55,8 qm
Zuwegungen	35,6 qm
Schuppen bei Terrassen	10,4 qm
Gartenschuppen	24,4 qm
Müllplatz (1/2)	8,2 qm
GR gesamt	=433,8 qm
GRZ 2	**=0,52**

Zeile 12.2-09 - 12.2-12
mit Gartenweg

Grundstück	830 qm
GR Hauptgebäude	251,5 qm
GRZ 1 Hauptgebäude	**=0,30**
GR Hauptgeb. + Terr.	=299,4 qm
GRZ Hauptgebäude + Terr.	**=0,36**
Stellplätze/Zufahrten	55,8 qm
Zuwegungen	35,6 qm
Schuppen bei Terrassen	10,4 qm
Gartenschuppen	24,4 qm
Müllplatz (1/2)	8,2 qm
Gartenweg	33,0 qm
GR gesamt	=466,8 qm
GRZ 2	**=0,56**

Projekt

Lübeck-Travemünde
Bebauungsplan 32.61.00
"Neue Teutendorfer Siedlung"

Planinhalt:

Reihenhäuser BF 12.2
Typ ERH 5,00m/MRH 6,00m
GRZ-Plan
Hs. 12.2-06 - Hs. 12.2-12

Bauherr:

bpd
bouwfonds immobilienentwicklung

BPD Immobilienentwicklung GmbH
Region Nord
Winterstraße 2; 22765 Hamburg;
Tel.: +49 40 68 87 68-0
hamburg@bpd-de.de

.....
Unterschrift

Planverfasser:

PWS

Planungsgesellschaft Weber - Schmetzer mbH
Hinrich-Thieß-Straße 46e; D-22844 Norderstedt;
Tel.: (040) 526 82 771; pws@wtnet.de

.....
Unterschrift

Phase	Bereich	Teil	Index
100 - Konzept	**12.2**	**2a**	s.u.

Datum 23.05.2024
Index:
a
b
c
Maßstab/Größe: M 1:100 / 59,4x59,4

0 1 2 3 4 5 10 m

Variante B:
Gartenweg bei 3 Häusern hinter 0,8m-Hecke zzg. 2,20m
Grünstreifen hinter dem Weg (d.h. bei 6 von 12 Häusern/Zeile)

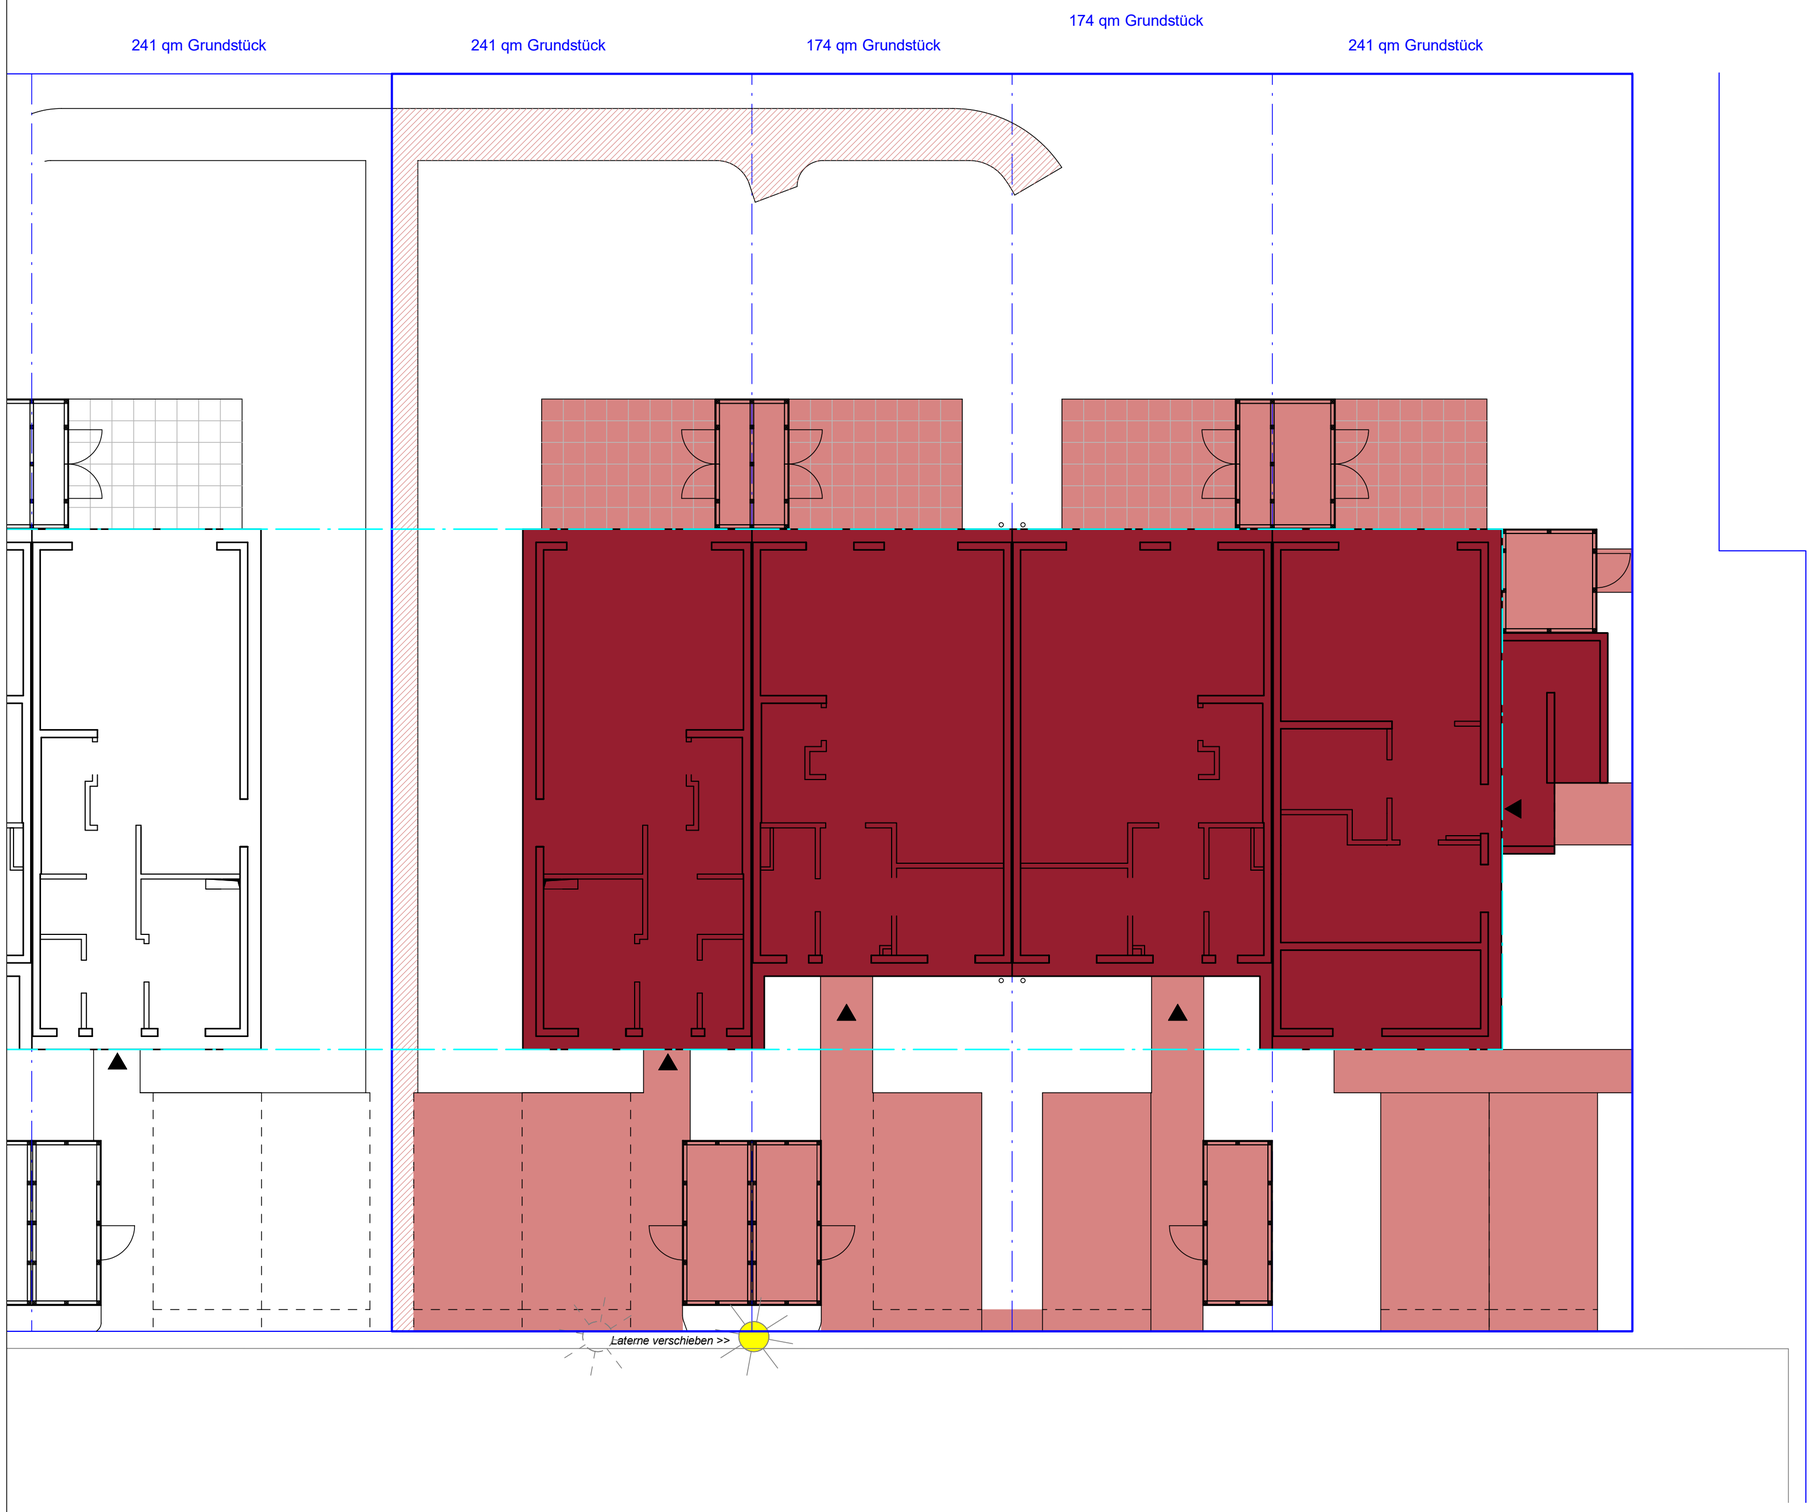

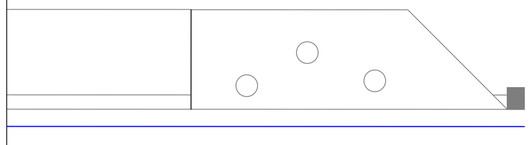

Grundstück	241 qm
GR Hauptgebäude	63,4 qm
GRZ 1 Hauptgebäude	**=0,26**
GR Hauptgebäude + Terr.	=75,4 qm
GRZ Hauptgebäude + Terr.	**=0,31**
Stellplätze/Zufahrt	27,5 qm
Zuwegung	7,9 qm
Schuppen bei Terrasse	2,6 qm
Gartenschuppen	6,1 qm
GR gesamt	=119,5 qm
GRZ 2	**=0,50**

Grundstück	174 qm
GR Hauptgebäude	62,3 qm
GRZ 1 Hauptgebäude	**=0,36**
GR Hauptgebäude + Terr.	=74,3 qm
GRZ Hauptgebäude + Terr.	**=0,43**
Stellplatz/Zufahrt	14,1 qm
Zuwegung	9,9 qm
Schuppen bei Terrasse	2,6 qm
Gartenschuppen	6,1 qm
GR gesamt	=107,0 qm
GRZ 2	**=0,615**

Grundstück	174 qm
GR Hauptgebäude	62,3 qm
GRZ 1 Hauptgebäude	**=0,36**
GR Hauptgebäude + Terr.	=74,3 qm
GRZ Hauptgebäude + Terr.	**=0,43**
Stellplatz/Zufahrt	14,1 qm
Zuwegung	9,9 qm
Schuppen bei Terrasse	2,6 qm
Gartenschuppen	6,1 qm
GR gesamt	=107,0 qm
GRZ 2	**=0,615**

Grundstück	241 qm
GR Hauptgebäude	73,9 qm
GRZ 1 Hauptgebäude	**=0,31**
GR Hauptgebäude + Terr.	=85,9 qm
GRZ Hauptgebäude + Terr.	**=0,36**
Stellplätze/Zufahrt	27,5 qm
Zuwegungen	10,3 qm
Schuppen bei Terrasse	2,6 qm
Gartenschuppen	5,3 qm
GR gesamt	=131,3 qm
GRZ 2	**=0,55**

Zeile 12.2-09 - 12.2-12
ohne Gartenweg

Grundstück	830 qm
GR Hauptgebäude	261,9 qm
GRZ 1 Hauptgebäude	**=0,32**
GR Hauptgeb. + Terr.	=308,4 qm
GRZ Hauptgebäude + Terr.	**=0,37**
Stellplätze/Zufahrten	83,2 qm
Zuwegungen	38,1 qm
Schuppen bei Terrassen	12,2 qm
Gartenschuppen	23,6 qm
GR gesamt	=467,0 qm
GRZ 2	**=0,56**

Zeile 12.2-09 - 12.2-12
mit Gartenweg

Grundstück	830 qm
GR Hauptgebäude	261,9 qm
GRZ 1 Hauptgebäude	**=0,32**
GR Hauptgeb. + Terr.	=308,4 qm
GRZ Hauptgebäude + Terr.	**=0,37**
Stellplätze/Zufahrten	55,8 qm
Zuwegungen	35,6 qm
Schuppen bei Terrassen	12,2 qm
Gartenschuppen	23,6 qm
Gartenweg	35,0 qm
GR gesamt	=502,0 qm
GRZ 2	**=0,605**

Projekt

Lübeck-Travemünde
Bebauungsplan 32.61.00
"Neue Teutendorfer Siedlung"

Planinhalt:

Reihenhäuser BF 12.2
Typ ERH 5,00m/MRH 6,00m
GRZ-Plan
Hs. 12.2-01 - Hs. 12.2-04

Bauherr:

bpd
bouwfonds immobilienentwicklung

BPD Immobilienentwicklung GmbH
Region Nord
Winterstraße 2; 22765 Hamburg;
Tel.: +49 40 68 87 68-0
hamburg@bpd-de.de

.....
Unterschrift

Planverfasser:

PWS

Planungsgesellschaft Weber - Schmetzer mbH
Hinrich-Thieß-Straße 46e; D-22844 Norderstedt;
Tel.: (040) 526 82 771; pws@wtnet.de

.....
Unterschrift

Phase	Bereich	Teil	Index
100 - Konzept	**12.2**	**2b**	s.u.

Datum 23.05.2024
Index:
a
b
c
Maßstab/Größe: M 1:100 / 59,4x59,4

0 1 2 3 4 5 10 m