OG	**EG-**	Summe	**OG**	**EG-**	Summe
52,15qm	**Variante 1**	**=120,38qm**	52,15qm	**Variante 2**	**=119,84qm**
	60,73qm	+Spitzboden		60,19qm	+Spitzboden
	+15,0/2			+15,0/2	
	=7,50qm			=7,50qm	
	=65,23qm			=67,69qm	

Projekt

Lübeck-Travemünde
Bebauungsplan 32.61.00
"Neue Teutendorfer Siedlung"

Planinhalt:

Doppelhäuser BF 12.5
Typ DHH 6,80 x 11,80m
Grundrisse EG+OG
Hs. 12.5-01 - Hs. 12.5-04

Bauherr:

bpd
bouwfonds immobilienentwicklung

BPD Immobilienentwicklung GmbH
Region Nord
Winterstraße 2; 22765 Hamburg;
Tel.: +49 40 68 87 68-0
hamburg@bpd-de.de

.....
Unterschrift

Planverfasser:

PWS

Planungsgesellschaft Weber - Schmetzer mbH
Hinrich-Thieß-Straße 46e; D-22844 Norderstedt;
Tel.: (040) 526 82 771; pws@wtnet.de

.....
Unterschrift

Phase	Bereich	Teil	Index
100 - Konzept	**12.5**	**1**	s.u.

Datum 23.05.2024
Index:
a
b
c
Maßstab/Größe: M 1:100 / 59,4x59,4

0 1 2 3 4 5 10 m

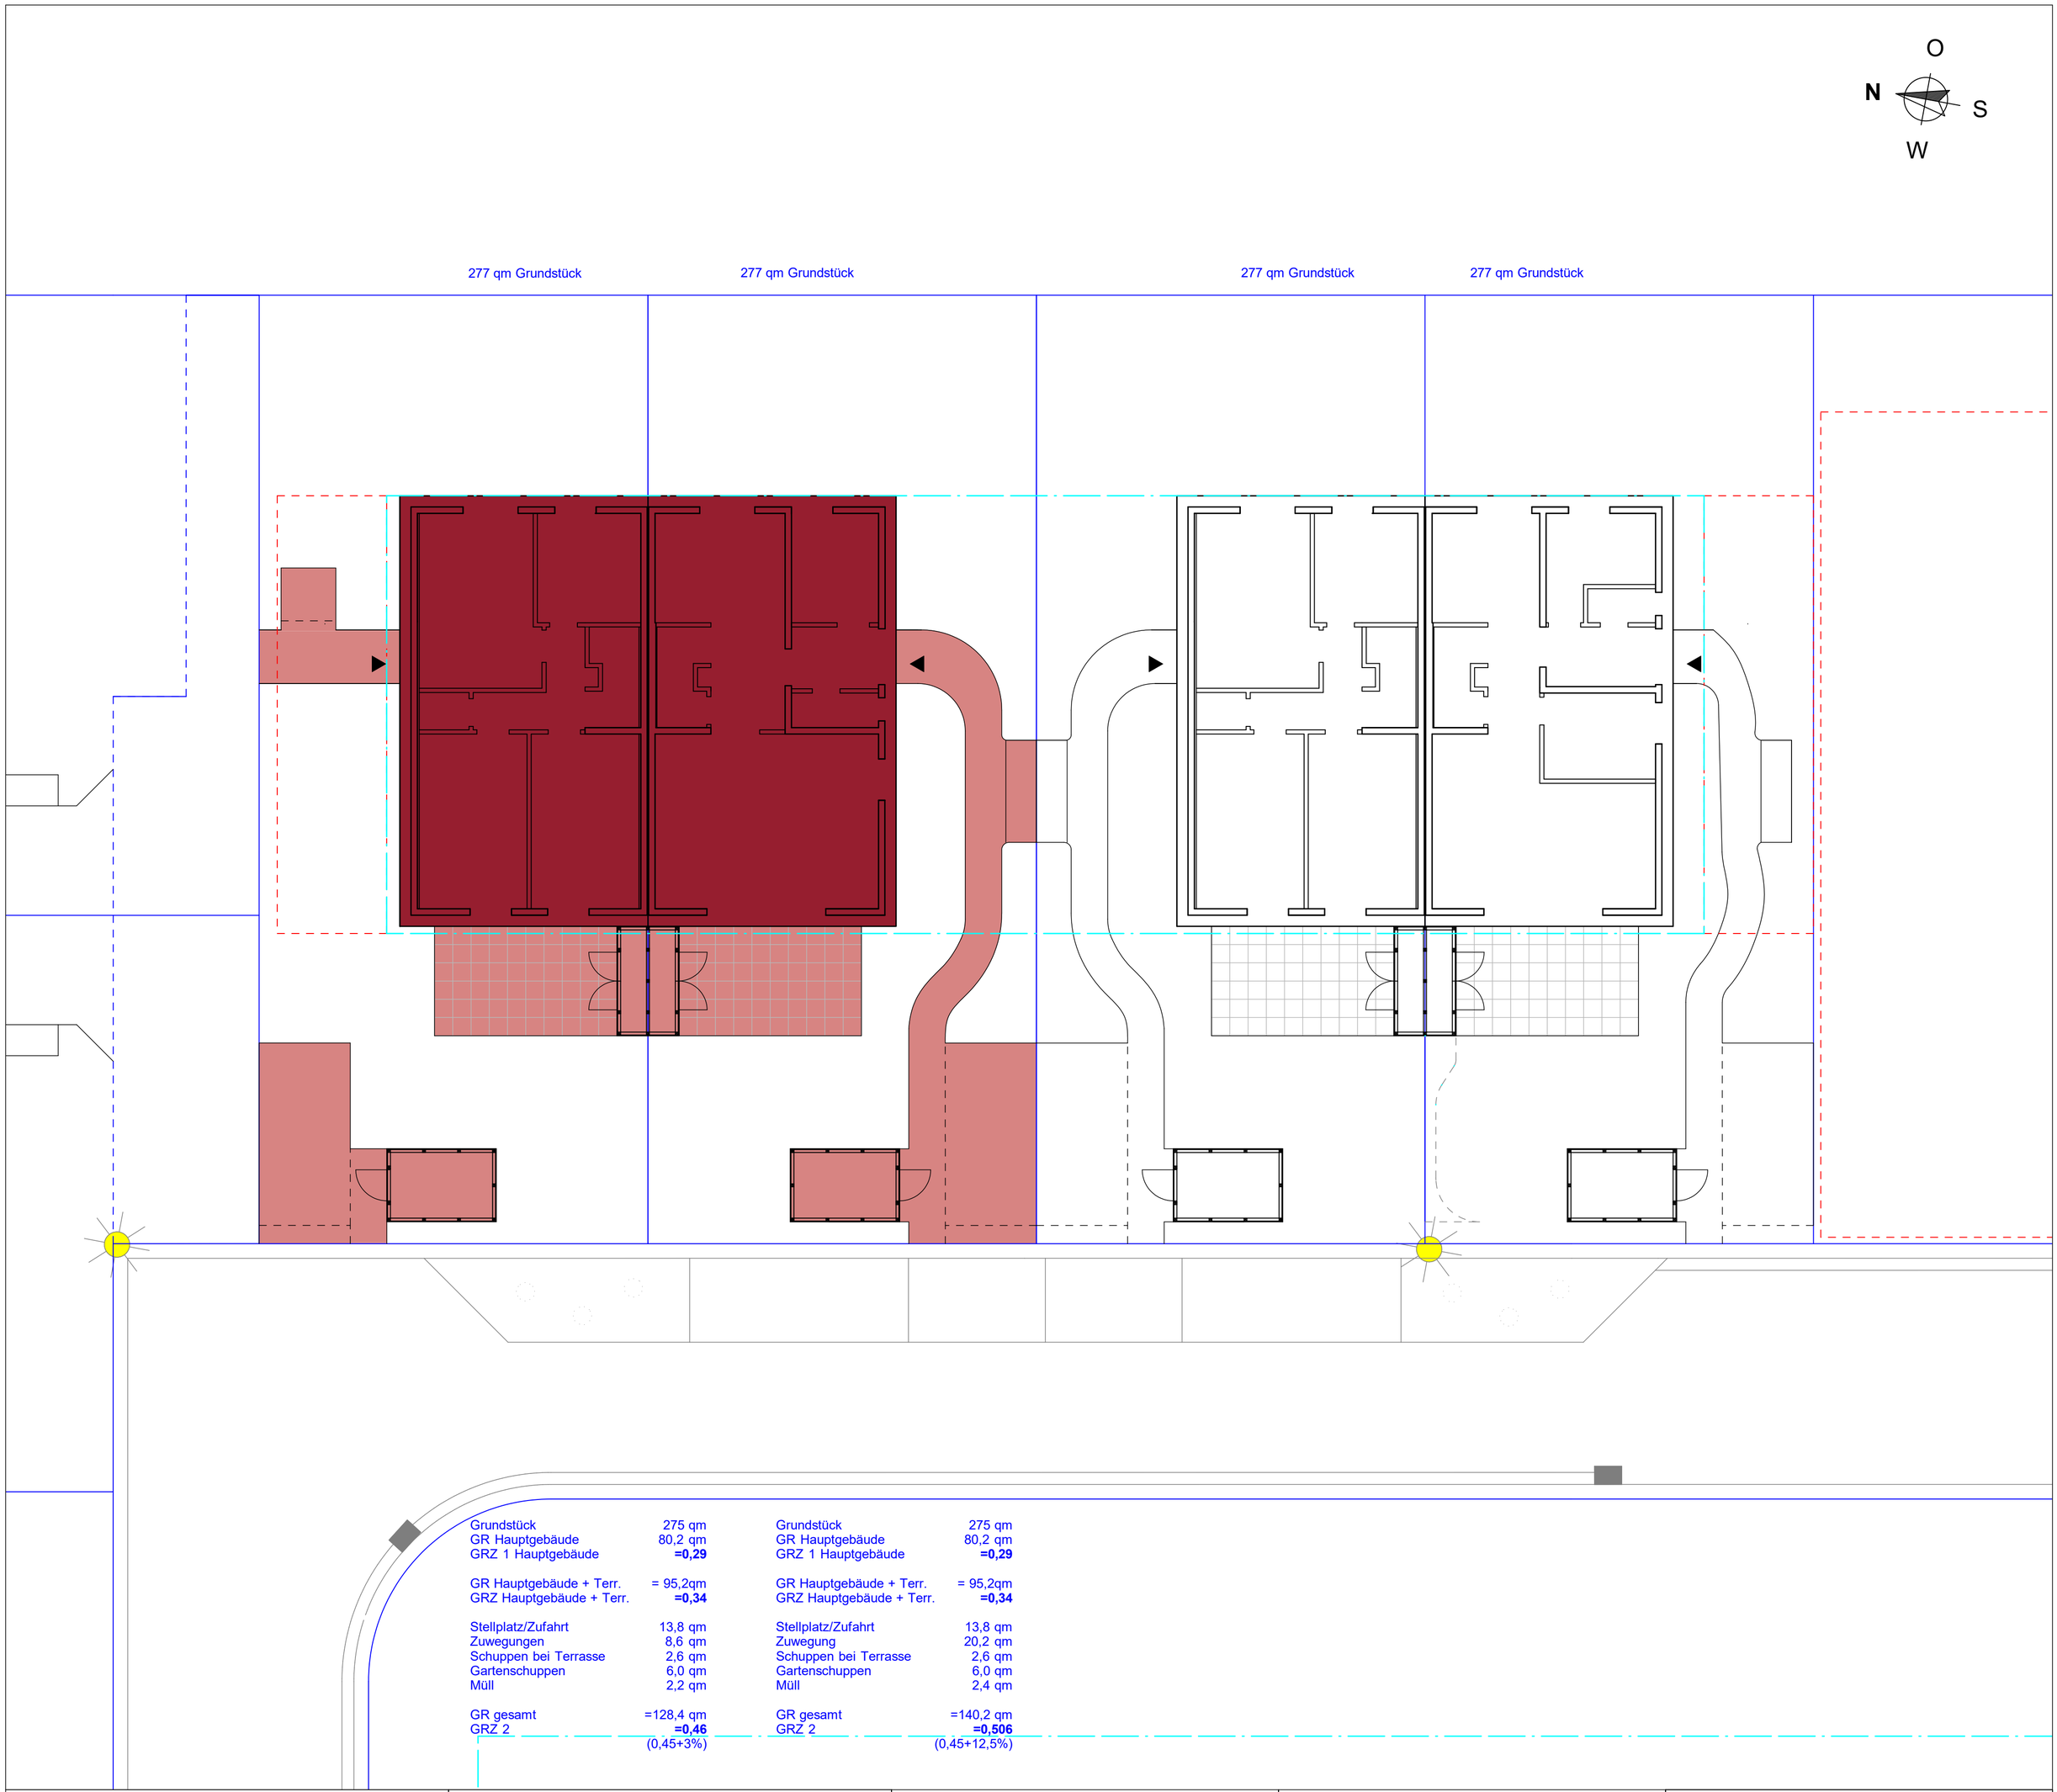

Grundstück	275 qm	Grundstück	275 qm
GR Hauptgebäude	80,2 qm	GR Hauptgebäude	80,2 qm
GRZ 1 Hauptgebäude	**=0,29**	GRZ 1 Hauptgebäude	**=0,29**
GR Hauptgebäude + Terr.	= 95,2qm	GR Hauptgebäude + Terr.	= 95,2qm
GRZ Hauptgebäude + Terr.	**=0,34**	GRZ Hauptgebäude + Terr.	**=0,34**
Stellplatz/Zufahrt	13,8 qm	Stellplatz/Zufahrt	13,8 qm
Zuwegungen	8,6 qm	Zuwegung	20,2 qm
Schuppen bei Terrasse	2,6 qm	Schuppen bei Terrasse	2,6 qm
Gartenschuppen	6,0 qm	Gartenschuppen	6,0 qm
Müll	2,2 qm	Müll	2,4 qm
GR gesamt	=128,4 qm	GR gesamt	=140,2 qm
GRZ 2	**=0,46**	GRZ 2	**=0,506**
	(0,45+3%)		(0,45+12,5%)

Projekt

Lübeck-Travemünde
Bebauungsplan 32.61.00
"Neue Teutendorfer Siedlung"

Planinhalt:

Doppelhäuser BF 12.5
Typ DHH 6,80 x 11,80m
GRZ-Plan
Hs. 12.5-01 - Hs. 12.5-04

Bauherr:

bpd
bouwfonds immobilienentwicklung

BPD Immobilienentwicklung GmbH
Region Nord
Winterstraße 2; 22765 Hamburg;
Tel.: +49 40 68 87 68-0
hamburg@bpd-de.de

.....
Unterschrift

Planverfasser:

PWS

Planungsgesellschaft Weber - Schmetzer mbH
Hinrich-Thieß-Straße 46e; D-22844 Norderstedt;
Tel.: (040) 526 82 771; pws@wtnet.de

.....
Unterschrift

Phase	Bereich	Teil	Index
100 - Konzept	**12.5**	**2**	s.u.

Datum 23.05.2024
Index:
a
b
c
Maßstab/Größe: M 1:100 / 59,4x59,4

0 1 2 3 4 5 10 m