Fenster bodentief,
Badfenster Brüstungsfenster ohne Unterlicht,
Fassadenmaterial angepasst,
Dach Staffelgeschoss angehoben

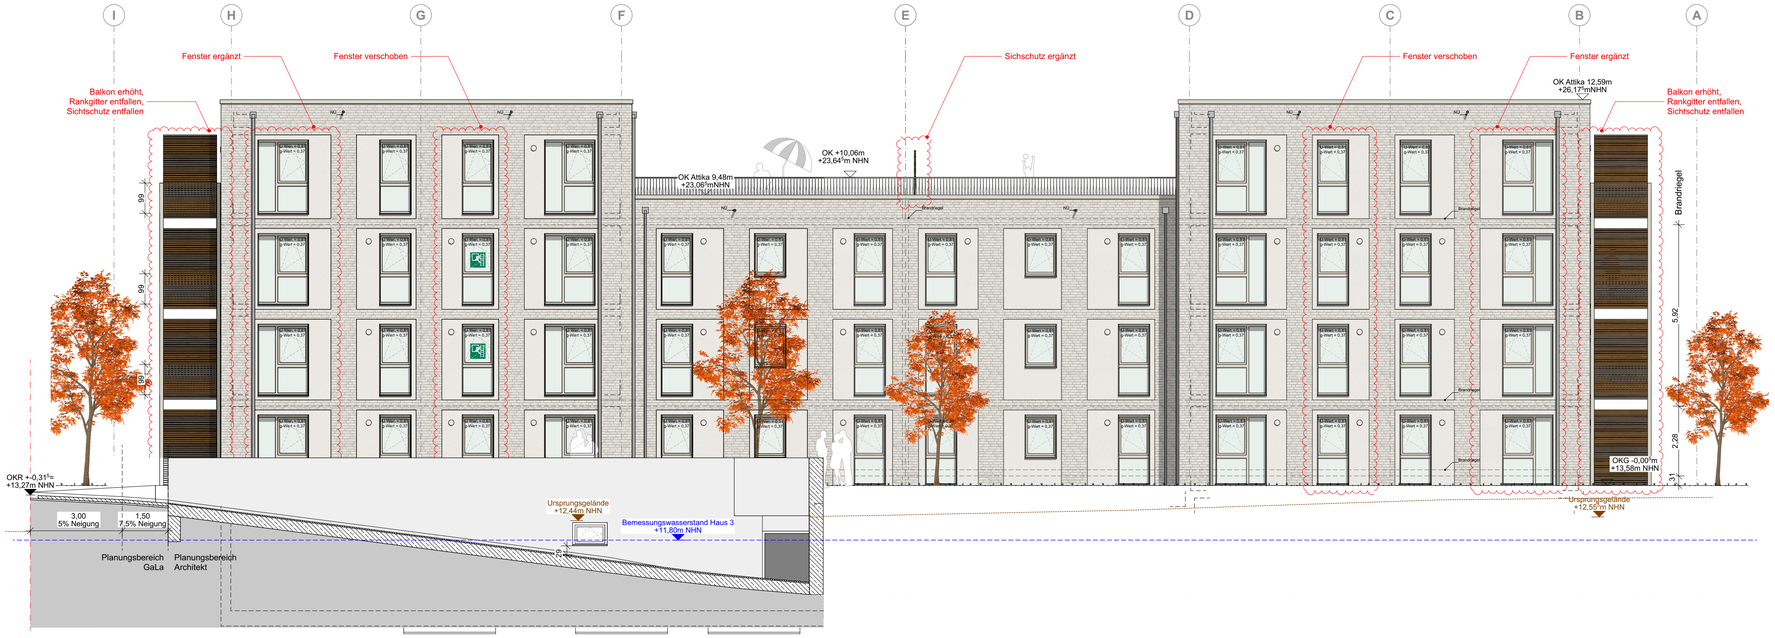

BAUNULL 003 = ±0,00 = 13,585m NHN

BRH	Brüstungshöhe ab OKFF	F/A	Fassadentür Alurohrrahmen	LB	lichte Breite	UK	Unterkante
D	Drehflügel	F/K	Fassadentür Kunststoff	OK	Oberkante	VK	Vorderkante
DF	Dehnungsfuge	F/S	Fassadentür Stahl	PU	Putz	WH	Wandhydrant
DK	Dreh-, Kippflügel	K	Kippflügel	RD	Rohrdecke	WU	wasserundurchlässig
FB	Fußbodenbelag	KL	Klapptflügel	RL	Rollladen	F	Feuerlöscher
FF	Fertigfußboden	LLi	im Lichten	RR	Regenfallrohr	NA	Notausgang
FV	Festverglasung	LH	lichte Höhe	SO	Sonnenschutz		

Erdreich

Rankgitter

Rettungsweg durch Anleitern mit tragbarer Leiter der Feuerwehr und geeignetes Fenster

Rettungsweg durch Anleitern mit Drehleiter der Feuerwehr und geeignetes Fenster

Achsen

Oberkante Ausbau

Oberkante Rohbau

Fassadenlüfter, Einbau verdeckt innerhalb der Laibung

Wandleuchte mit zweiseitigem Lichtaustritt

W1 WDVS Glatt, Farbton gem. Farb - und Materialkonzept

W2 WDVS Kammstruktur vertikal, Farbton gem. Farb - und Materialkonzept

F1 Fenster, Fensterbänke, Attikaabdeckung Farbton gem. Farb - und Materialkonzept

B1 Balkone Vorgestellt, Farbton gem. Farb - und Materialkonzept

G1 Balkon - und Dachterrassengeländer, Rankgitter Stahlgitter, Farbton gem. Farb - und Materialkonzept

INDEX:	ÄNDERUNGSINHALT:	DATUM:	GEZ.:
A	Planerstellung	11.12.2023	ys
B	Riemchen, Fasche um Fenster umlaufend, gedrehte Geländerstäbe, Änderungen gem. Anmerkungen	12.12.2025	ys

Die Pläne sind vom Auftragnehmer verantwortlich zu prüfen. Maße sind am Bau zu nehmen und zu kontrollieren. Eventuelle Differenzen zwischen den Plänen des Statikers, der Projektingenieure, der Fachfirmen und den Werkplänen des Architekten sind vor Ausführung der Arbeiten zu klären. Dieser Plan gilt nur in Verbindung mit den übrigen Ausführungsplänen des Architekten, den Plänen des Statikers, der Projektingenieure und der Fachfirmen. Baustoffe und Güteklassen sind der Statik zu entnehmen. Bedenken gegen die Konstruktion sind vor der Ausführung dem Architekten zu melden.

PROJEKT:

Neue Teutendorfer Siedlung 003

LEISTUNGSPHASE:

LP 4 - Genehmigungsplanung

BAUHERR:

BPD Immobilienentwicklung GmbH

Winterstraße 2
22765 Hamburg
Tel.: 040 / 68 87 68 0
hamburg@bpd-de.de
www.bpd-de

UNTERSCHRIFT:

DATUM:

ARCHITEKT:

Renner Hainke Wirth Zirn Architekten

Bernstorffstr. 69 22767 Hamburg
+49 (0) 40 - 431 352 40

www.rhwzarchitekten.de

UNTERSCHRIFT:

DATUM:

TRAGWERKSPLANUNG:

Ingenieurgesellschaft Dr. Apitz mbH
Platz der Freiheit 2-3
19053 Schwerin
Tel.: +49 385 760 42 13

GEBÄUDETECHNIK:

M.TGA Ingenieur GmbH
Mechower Weg 9
23911 Ziethen
Tel.: +49 4541 8858740

BRANDSCHUTZ:

Gruner Deutschland GmbH
Raboisen 16
20095 Hamburg
Tel.: 040 35 62 393 22

LANDSCHAFTSPLANUNG:

Clasen-Werning-Partner, Landschaftsarchitekten und Stadtplaner GmbH
Elisabeth-Haseloff-Str. 1
23564 Lübeck
Tel.: 0451 61 06 8 12

PLANINHALT:

Haus 3_Ansicht Nord

BLATTFORMAT: A1

MAßSTAB: 1:100

PLANKODIERUNG: Projekt_Baufeld_Haus_Planer_LPH_Planart_Planinhalt_Plannummer_Status_Index_Freitext

NTS_B03_003_ARC_4_AN_NX_002_F_B_Haus 3 Ansicht Nord

INDEX:

PLANNUMMER: 002

INDEXDATUM: 12.12.2025