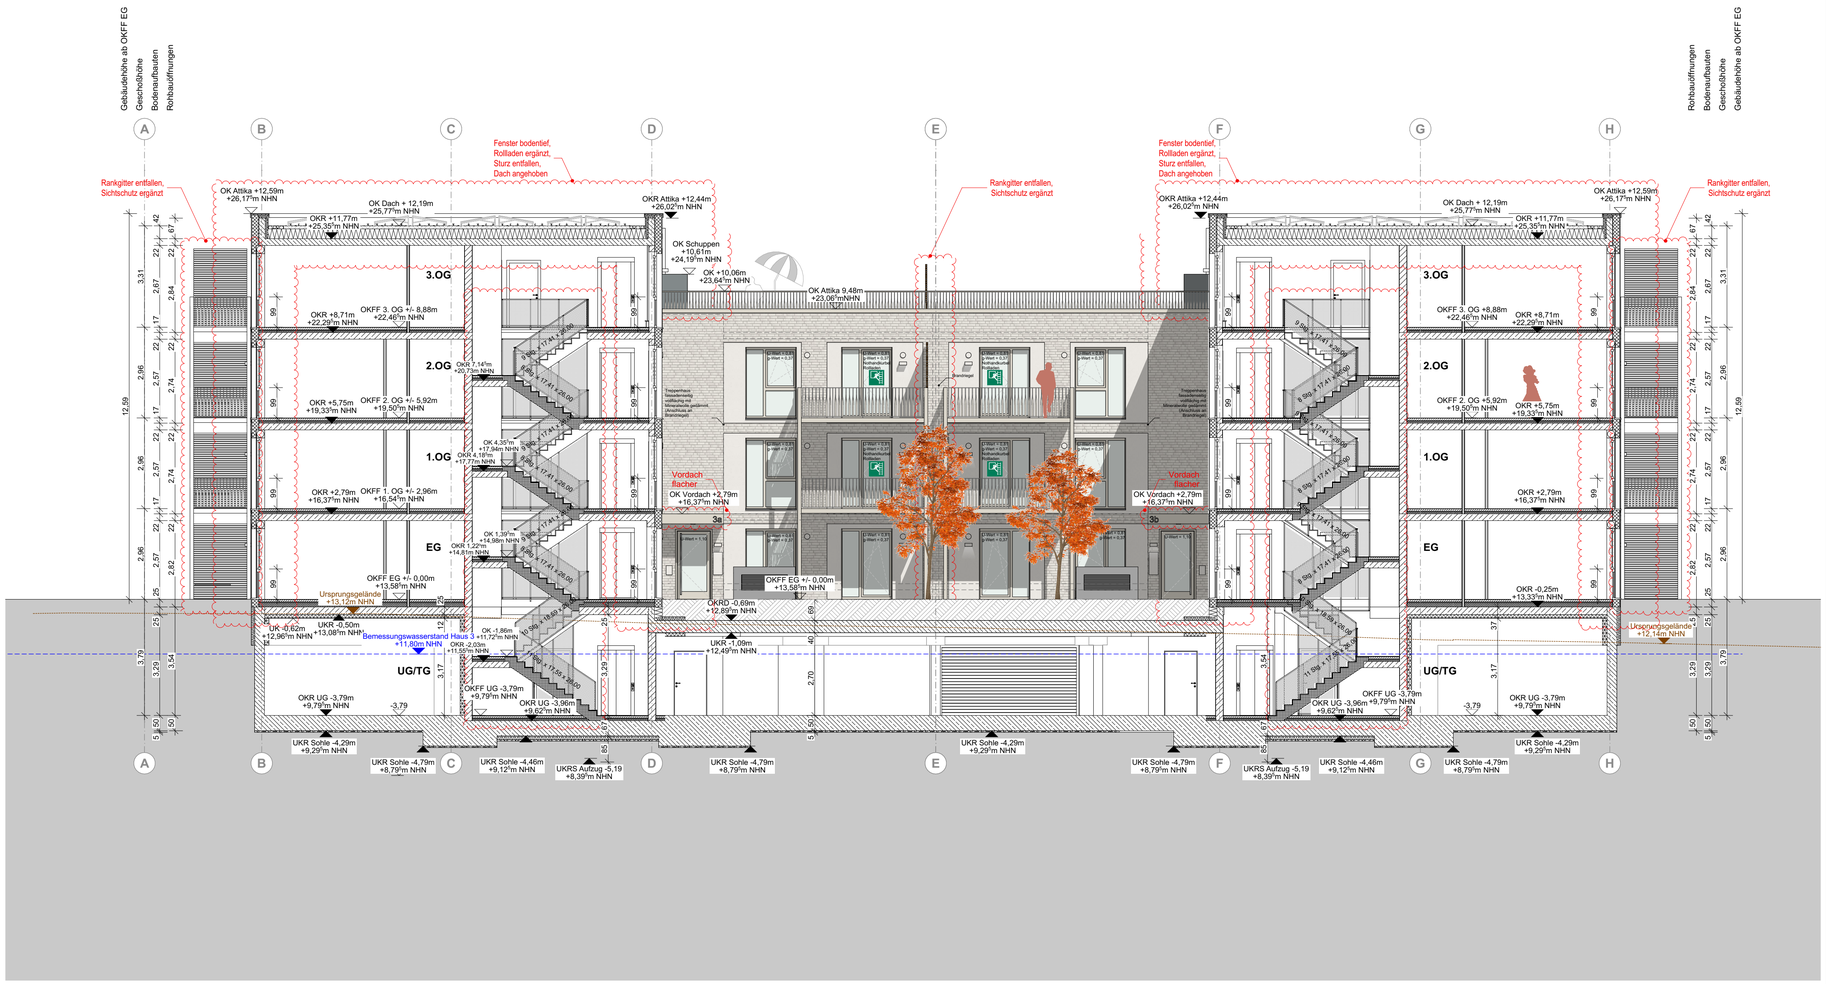

BAUNULL 003 = ±0,00 = 13,585m NHN

AHD	Abhangdecke	DSP	Deckenversprung	F30 (Fh)	feuerhemmend	RD	Rohdecke	UKF	Unterkante Fertig
BD	Brüstungsdurchbruch	ELV	Elektroverteilung	HKV	Heizkreisverteiler	RR	Regenfallrohr	UKR	Unterkante Roh
BRH	Brüstungshöhe ab OKFF	FF	Fertigfußboden	LLi	im Lichten	RS	Rauchschutztür	UV	Unterverteilung
BS	Bodenschlitz	F30/F90	Brandschutzanf. Wand	LH	lichte Höhe	T30/T90	Brandschutzanf. Tür	UZ	Unterzug
BW	Brandwand	F90 (Fb)	feuerbeständig	LB	lichte Breite	T90 (Fb)	feuerbeständig	ÜZ	Überzug
BBW	Bauart Brandwand	F90-M (Fb)	feuerbeständig und stoßfest	OK	Oberkante	T60 (hFh)	hoch feuerhemmend	VK	Vorderkante
DD	Deckendurchbruch	F60 (hFh)	hoch feuerhemmend	OKF	Oberkante Fertig	T30 (Fh)	feuerhemmend	WD	Wanddurchbruch
DS	dichtschließend	F60-M (hFh)	hoch feuerhemmend und stoßfest	OKR	Oberkante Roh	T30-RS	Rauchschutztür feuerhemmend	WS	Wandschlitz
				PV	Photovoltaik	UK	Unterkante	WU	wasserundurchlässig

WU-Stahlbeton		Trockenbauwand		Sichtschutz Freifläche	
Stahlbeton		WD Wanddurchbruch		Alternativ Einbau Badewanne	
Beton unbewehrt		Deckendurchbruch		Abhangdecke	
Estrich		Bodendurchbruch	UV	UV + HKV	
Mauerwerk KLB		Oberkante Ausbau		Push / Pull Lüfter	
XPS Hartschaumdämmplatte		Oberkante Rohbau		Rankgitter	
EPS Hartschaumdämmplatte		Achsen		Planänderung	
Holzwolle		Schnittlinien	B.	Barrierefreie Wohnung gem. §50 LBO	
Mineralwolle		Grundstücksgrenze			
		Außenzapfstelle			

INDEX:	ÄNDERUNGSINHALT:	DATUM:	GEZ.:
A	Planerstellung	11.12.2023	ys
B	Handlauf durchgehend, Vergrößerung Treppenpodest, Änderungen gem. Anmerkungen	12.12.2025	ys

Die Pläne sind vom Auftragnehmer verantwortlich zu prüfen. Maße sind am Bau zu nehmen und zu kontrollieren. Eventuelle Differenzen zwischen den Plänen des Statikers, der Projektingenieure, der Fachfirmen und den Werkplänen des Architekten sind vor Ausführung der Arbeiten zu klären. Dieser Plan gilt nur in Verbindung mit den übrigen Ausführungsplänen des Architekten, den Plänen des Statikers, der Projektingenieure und der Fachfirmen. Baustoffe und Güteklassen sind der Statik zu entnehmen. Bedenken gegen die Konstruktion sind vor der Ausführung dem Architekten zu melden.

PROJEKT:

Neue Teutendorfer Siedlung 003

LEISTUNGSPHASE:

LP 4 - Genehmigungsplanung

BAUHERR:

bpd

BPD Immobilienentwicklung GmbH

Winterstraße 2
22765 Hamburg
Tel.: 040 / 68 87 68 0
hamburg@bpd-de.de
www.bpd-de

UNTERSCHRIFT:

DATUM:

ARCHITEKT:

RENNER HAINKE WIRTH ZIRN Architekten

Renner Hainke Wirth Zirn Architekten

Bernstorffstr. 69 22767 Hamburg
+49 (0) 40 - 431 352 40

www.rhwzarchitekten.de

UNTERSCHRIFT:

DATUM:

TRAGWERKSPLANUNG:	GEBÄUDETECHNIK:	BRANDSCHUTZ:	LANDSCHAFTSPLANUNG:
Ingenieurgesellschaft Dr. Apitz mbH Platz der Freiheit 2-3 19053 Schwerin Tel.: +49 385 760 42 13	M.TGA Ingenieur GmbH Mechower Weg 9 23911 Ziethen Tel.: +49 4541 8858740	Gruner Deutschland GmbH Raboisen 16 20095 Hamburg Tel.: 040 35 62 393 22	Clasen-Werning-Partner, Landschaftsarchitekten und Stadtplaner GmbH Elisabeth-Haselhoff-Str. 1 23564 Lübeck Tel.: 0451 61 06 8 12

PLANINHALT:

Haus 3_Schnitt B-B

BLATTFORMAT: A1

MAßSTAB: 1:100

PLANKODIERUNG: Projekt_Baufeld_Haus_Planer_LPH_Planart_Planinhalt_Plannummer_Status_Index_Freitext

NTS_B03_003_ARC_4_SC_22_001_F_B_Haus 3 Schnitt B-B

INDEX:

PLANNUMMER: 001

INDEXDATUM: 12.12.2025